


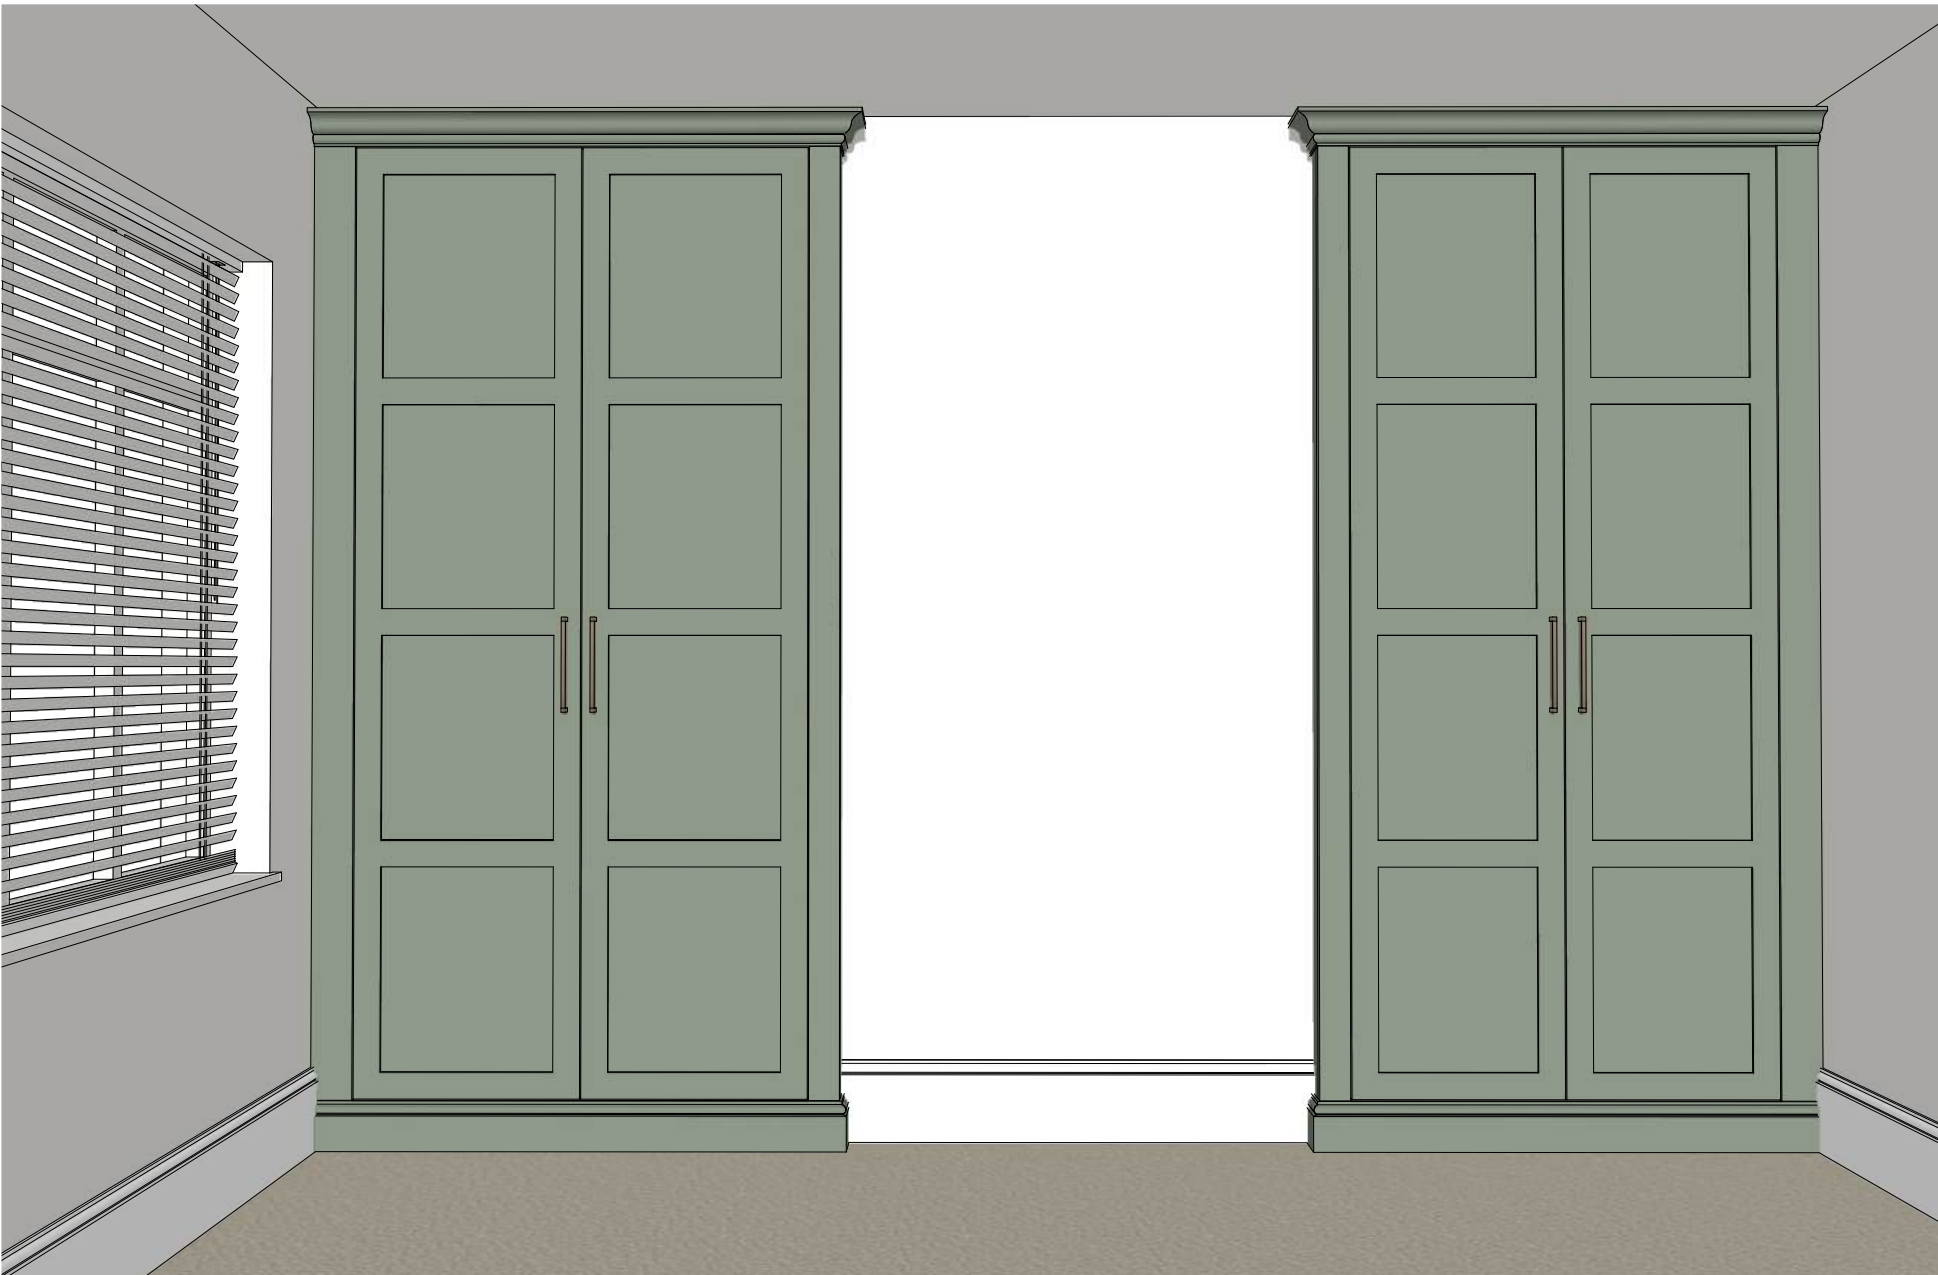

Client: Glen & Micheal	
Project: 1259 SPARE ROOM	
Drawing Title: 3D VIEW	
Date of first issue: 15 03 23	
Revision -	Dimensions: MM
Drawn by: MF	Page: 1
Revision details:	
	
wardsmithinteriors.co.uk	



HANDLE PLANK BECKER 230MM
EXTERNAL FINISH EGGER REED GREEN
INTERIOR FINISH OAK TBC

FRONT VIEW-1:25@A3




CIAIRO TRADITIONAL 4 PANEL SHAKER DOORS

FRONT VIEW-INTERNAL 1:25@A3

HIGH STORAGE
LONG HANGING
ADJUSTABLE SHELVING




SHELVING FIXED
DIMMABLE LED LIGHTING
PULL OUT DESK

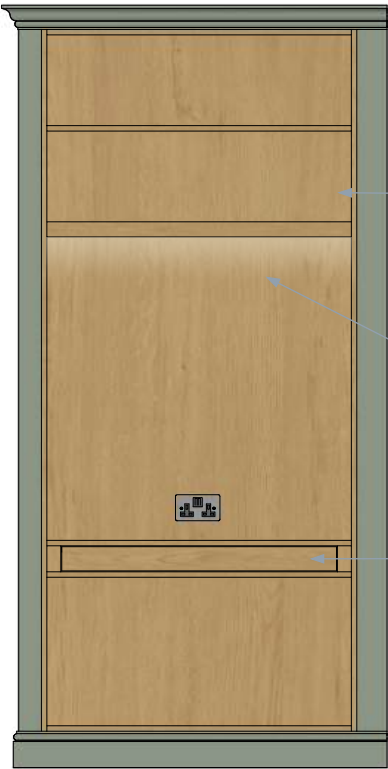


Client: Glen & Micheal	
Project: 1259 SPARE ROOM	
Drawing Title: GA DETAILS	
Date of first issue: 15 03 23	
Revision -	Dimensions: MM
Drawn by: MF	Page: 2
Revision details:	
wardsmithinteriors.co.uk	


TOP VIEW 1:25@A3

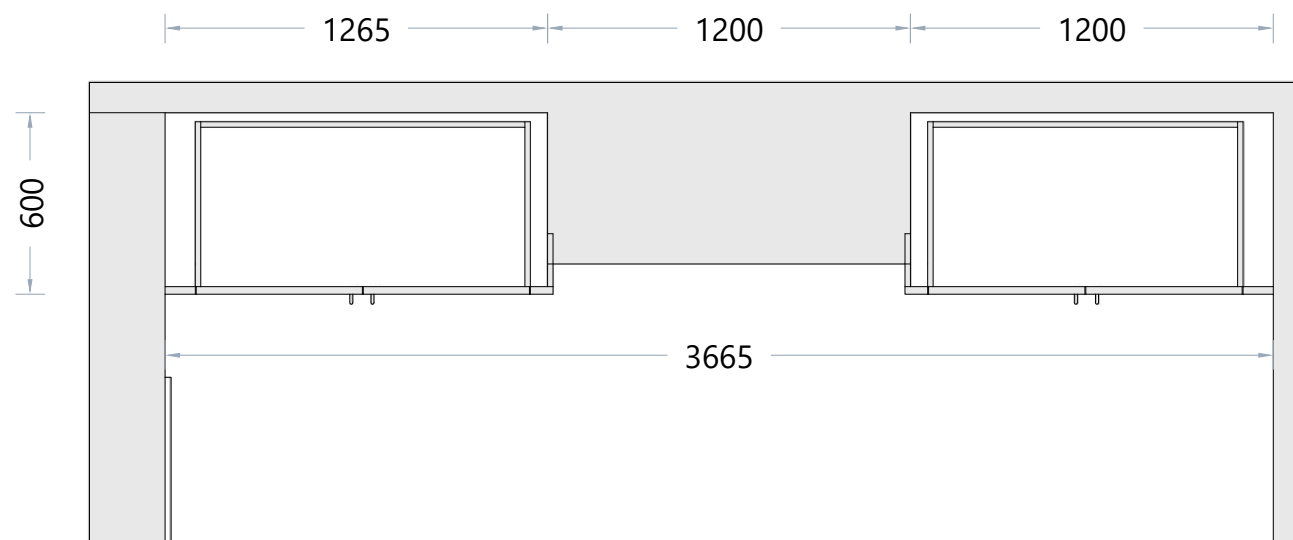

FRONT VIEW 1:25@A3

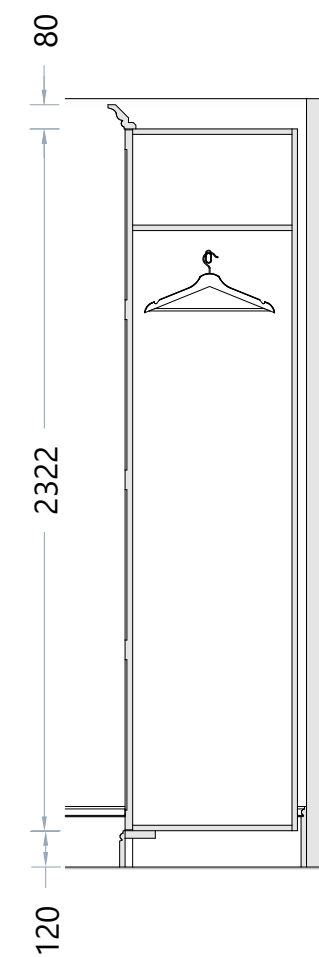

SECTION THROUGH LH UNIT
1:25@A3

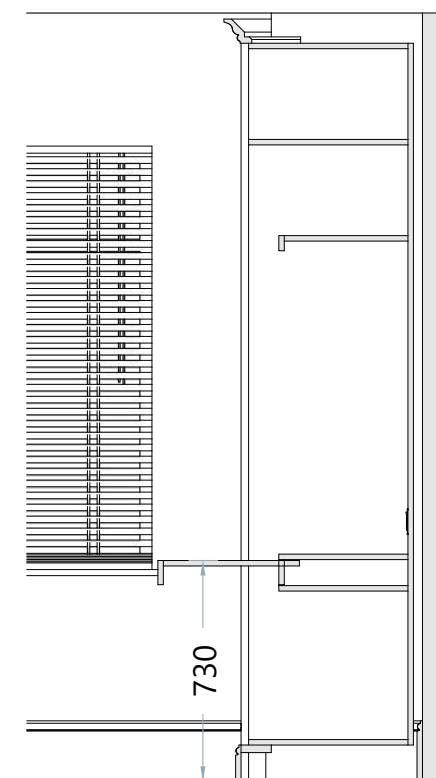

SECTION THROUGH RH UNIT
1:25@A3

Client:

Glen & Micheal

Project:

1259 SPARE ROOM

Drawing Title:

FULL ASSEMBLY DETAILS

Date of first issue:

15 03 23

Revision
-

Dimensions:
MM

Drawn by:
MF




Page:
3

Revision details:





wardsmithinteriors.co.uk


TOP VIEW 1:25@A3

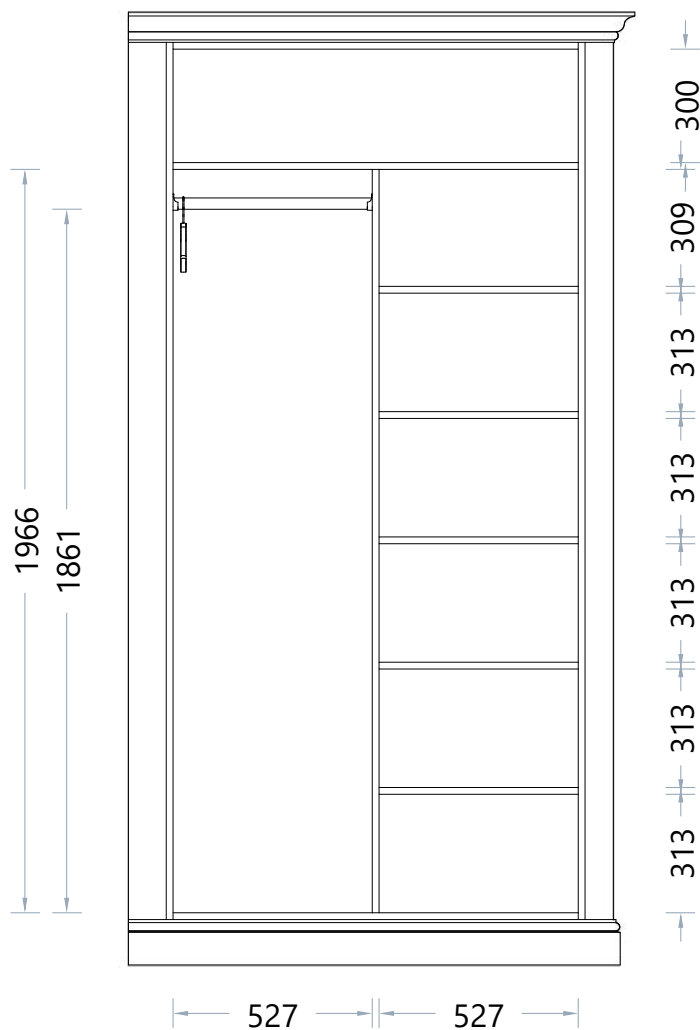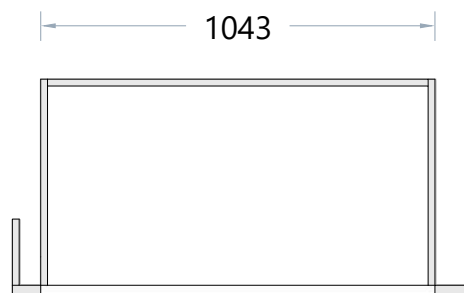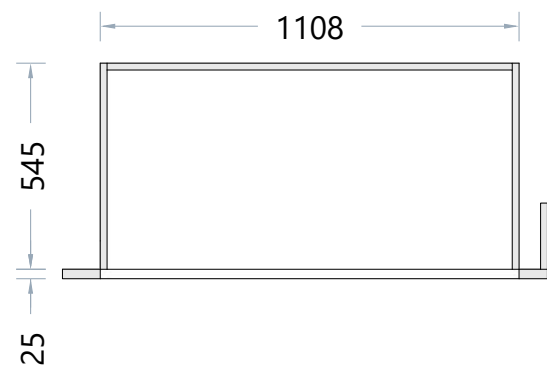

FRONT VIEW 1:25@A3

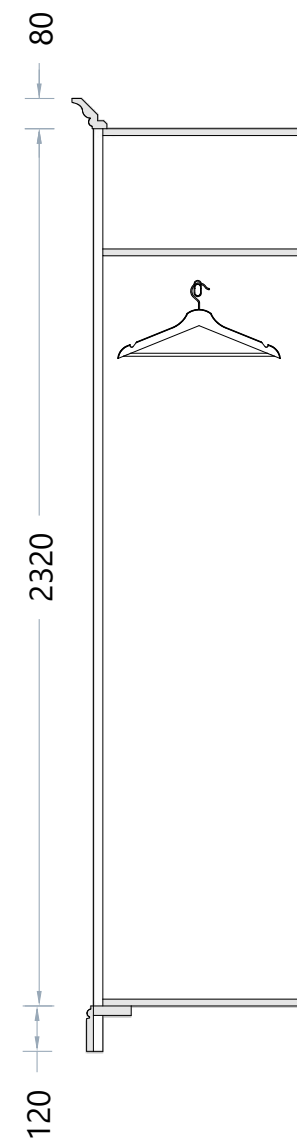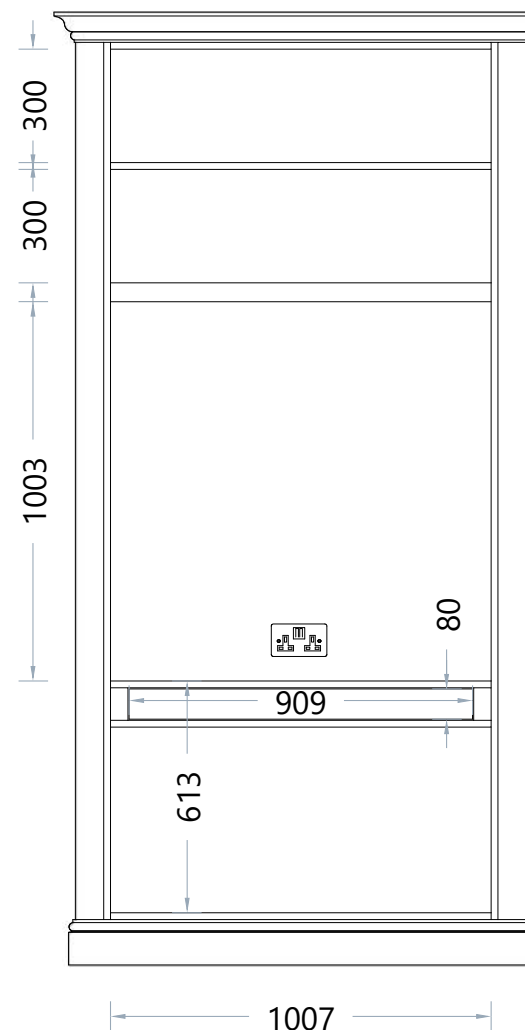

SECTION THROUGH LH UNIT
1:25@A3

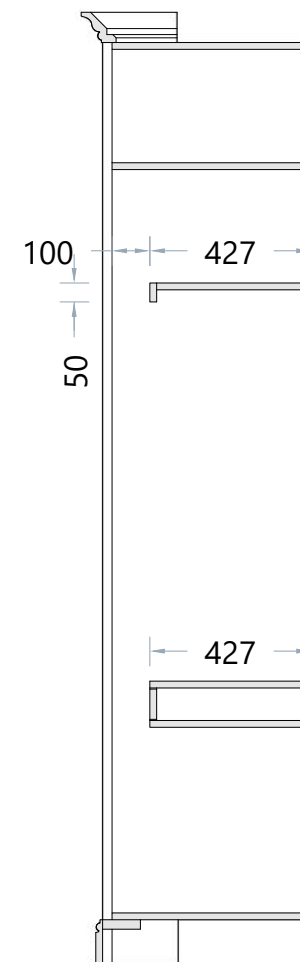

SECTION THROUGH RH UNIT
1:25@A3

Client: Glen & Micheal	
Project: 1259 SPARE ROOM	
Drawing Title: INTERNAL DETAILS	
Date of first issue: 15 03 23	
Revision -	Dimensions: MM
Drawn by: MF	Page: 4
Revision details:	
 wardsmithinteriors.co.uk	